




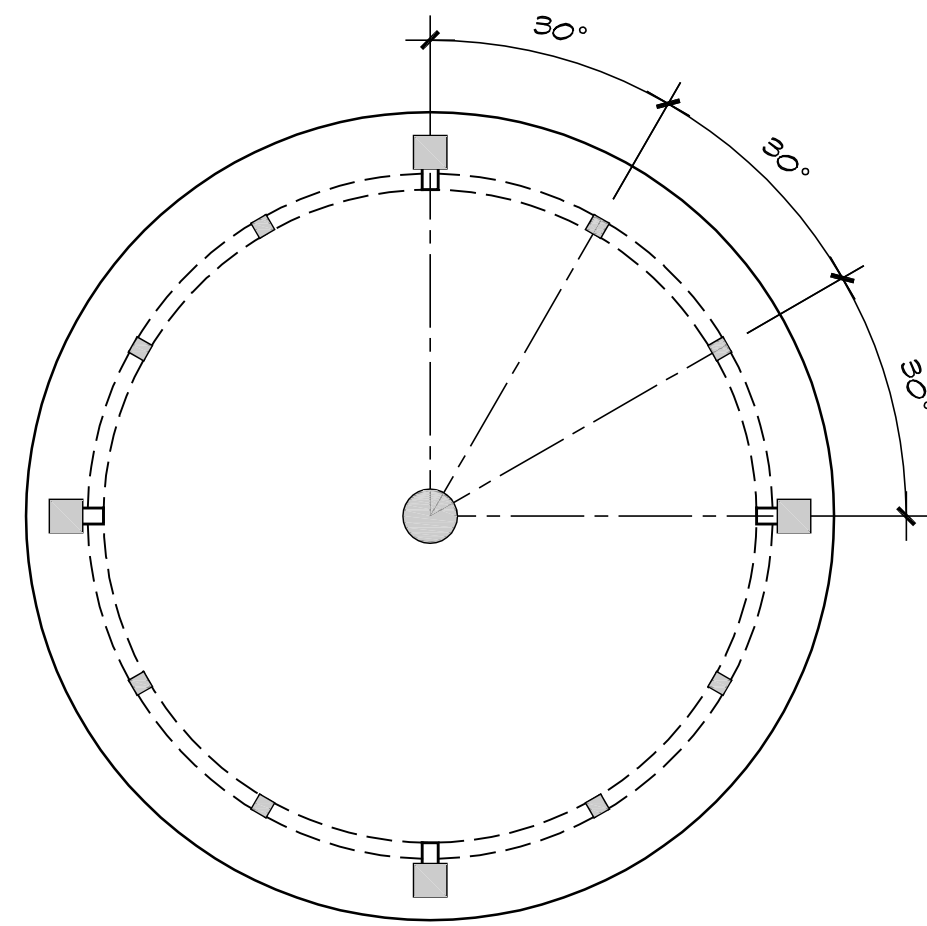


15 SPACER PLAN
SCALE: 1/2" = 1'-0"

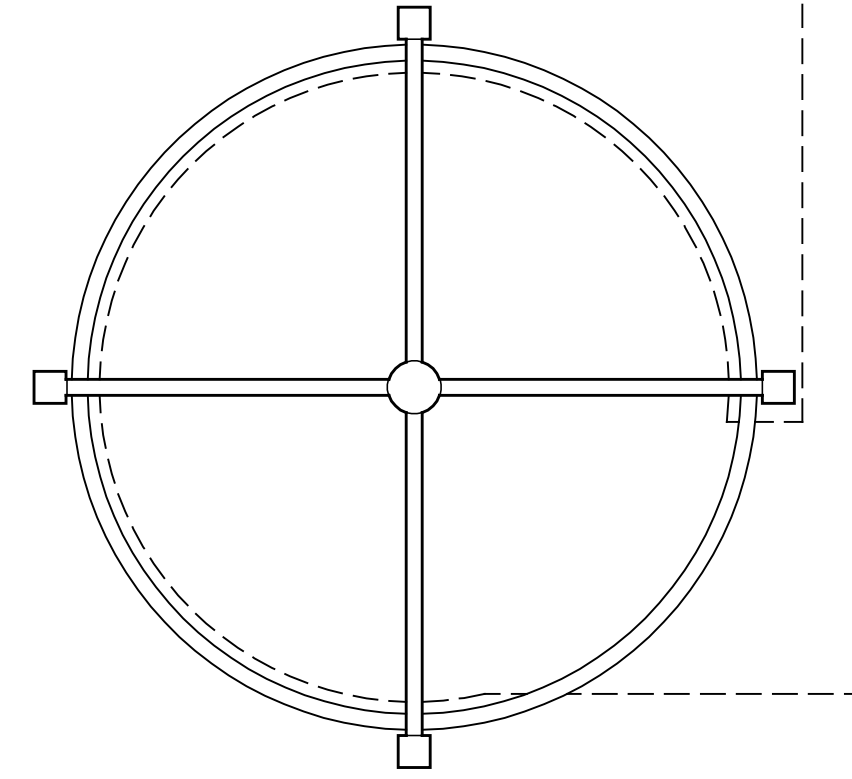


14 OPEN ROOF PLAN
SCALE: 1/2" = 1'-0"

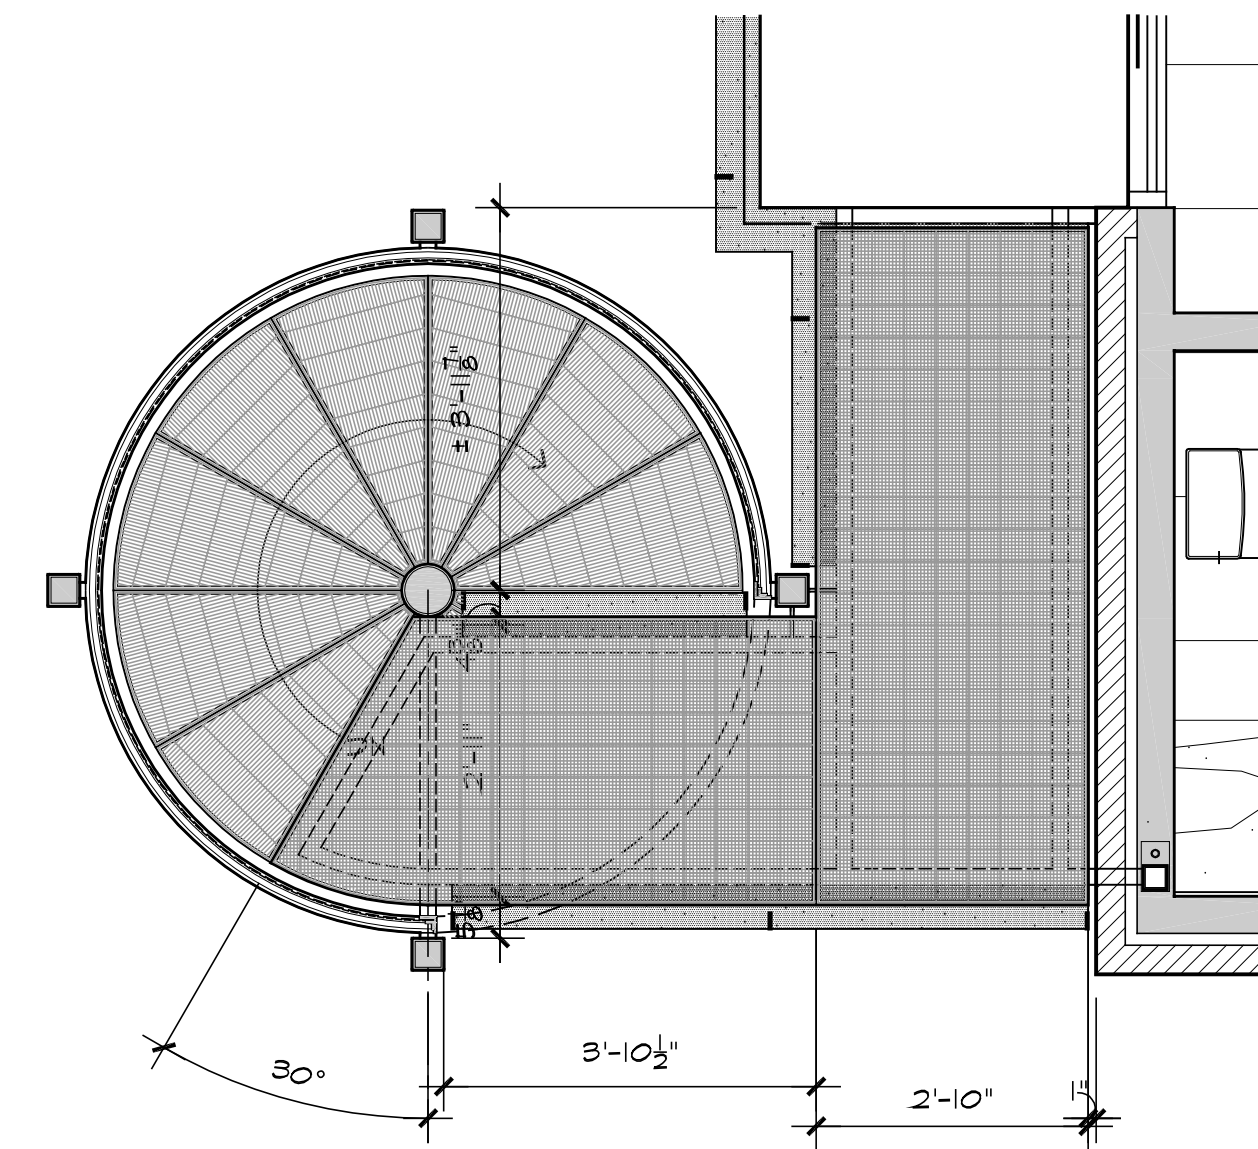


13 SECOND FLOOR PLAN
SCALE: 1/2" = 1'-0"

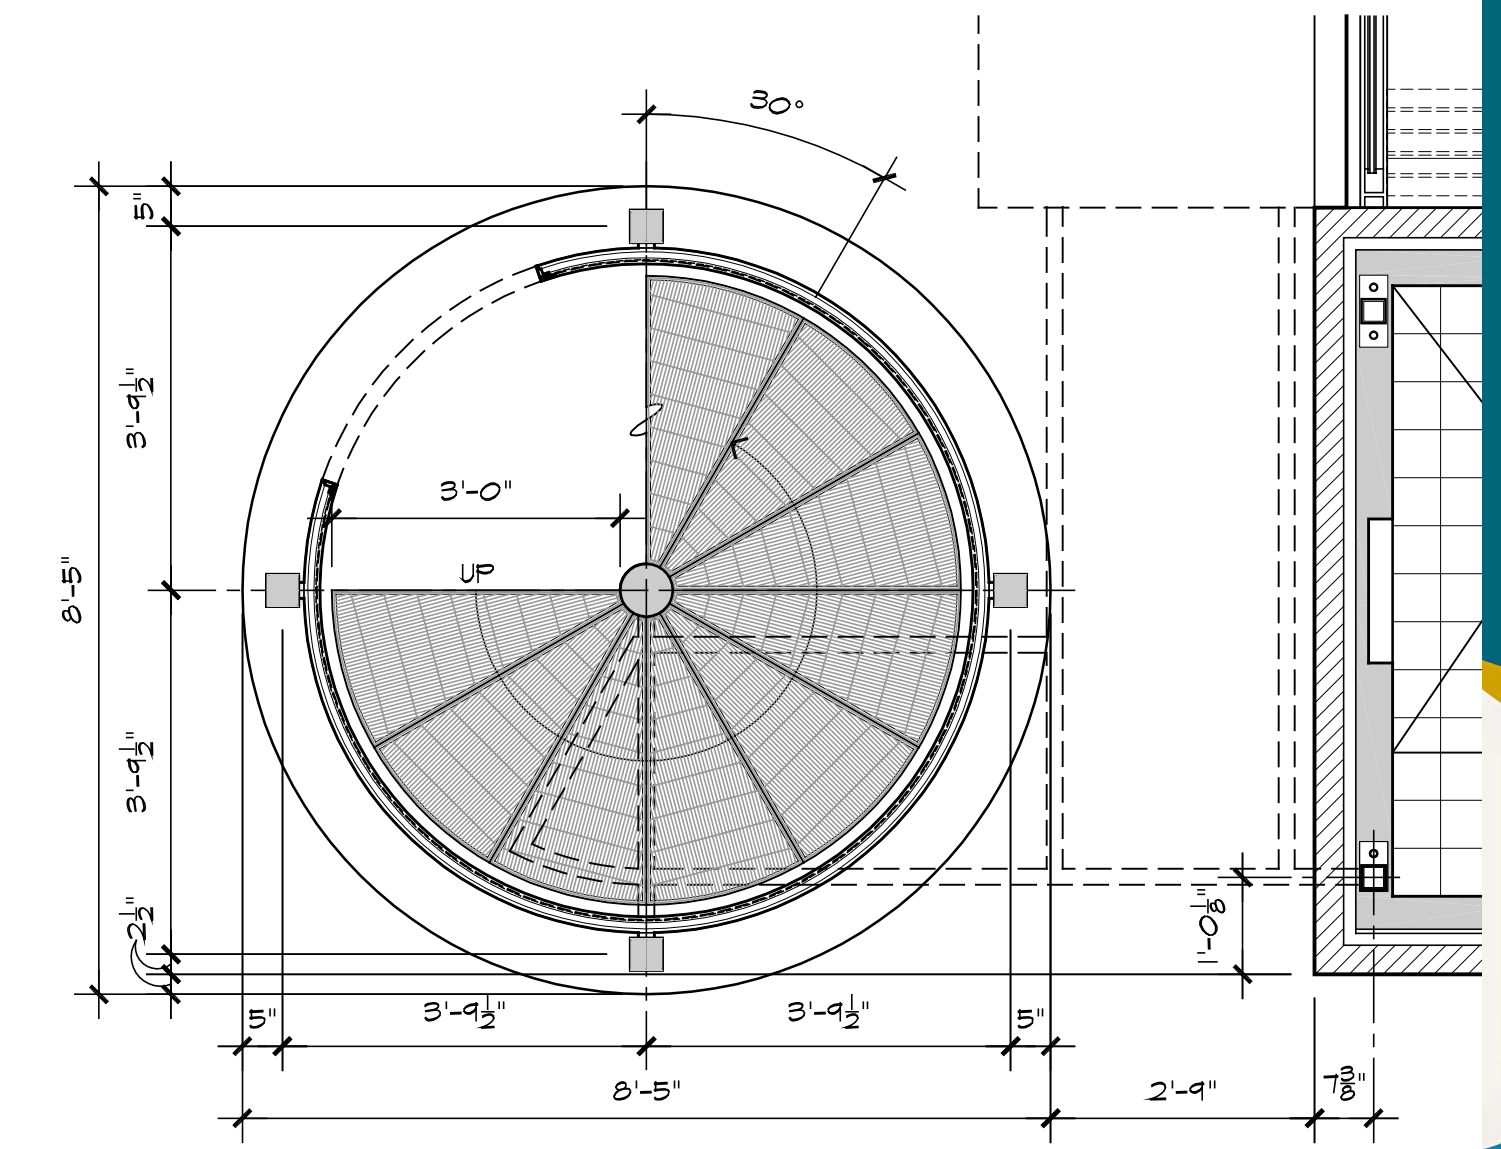


12 FIRST FLOOR PLAN
SCALE: 1/2" = 1'-0"

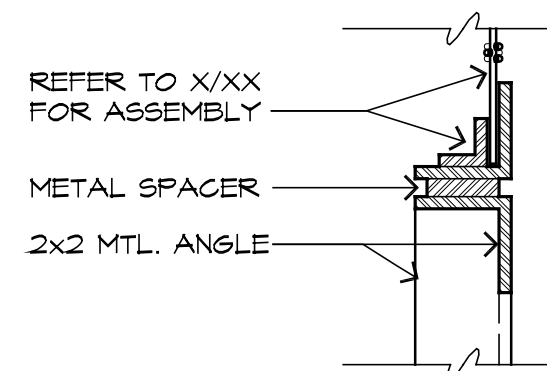


11 DETAIL
SCALE: 3" = 1'-0"

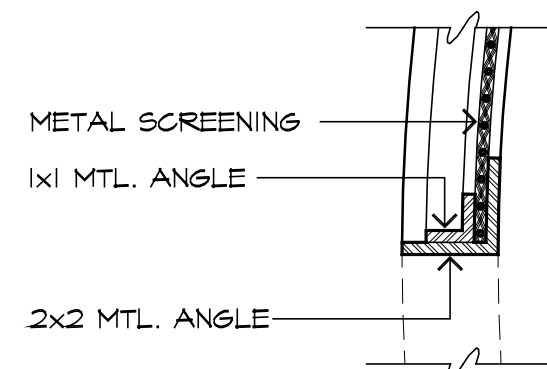


10 DETAIL
SCALE: 3" = 1'-0"

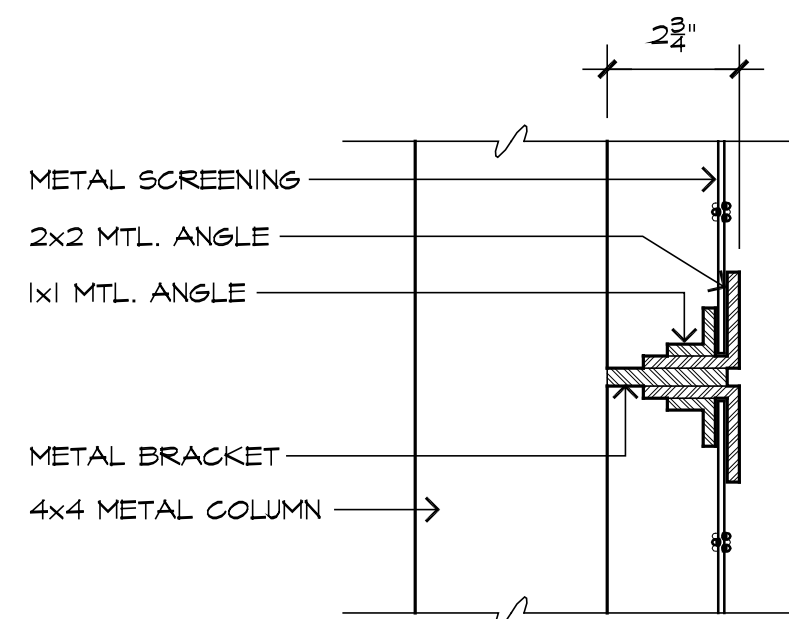


9 STAIR TREAD PLAN
SCALE: 3" = 1'-0"

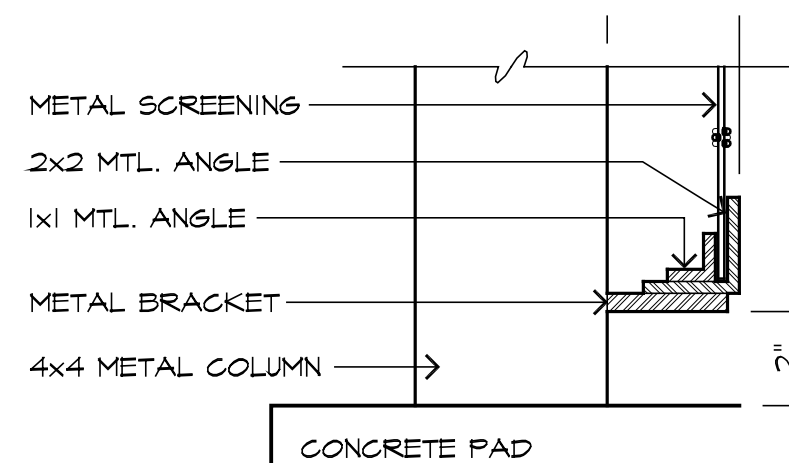


8 STAIR TREAD PLAN
SCALE: 3" = 1'-0"

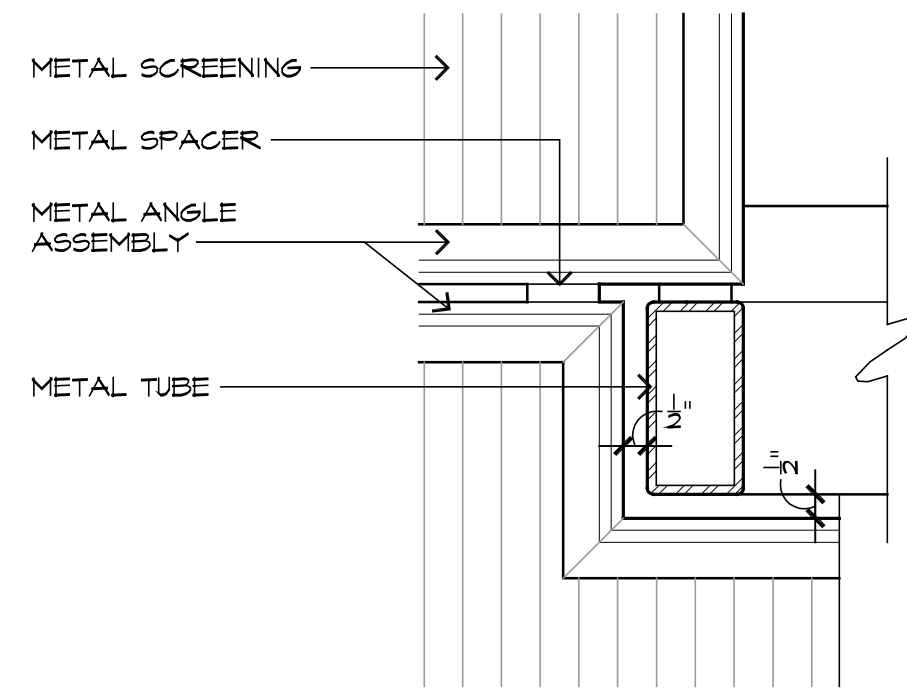


7 STAIR TREAD PLAN
SCALE: 3" = 1'-0"

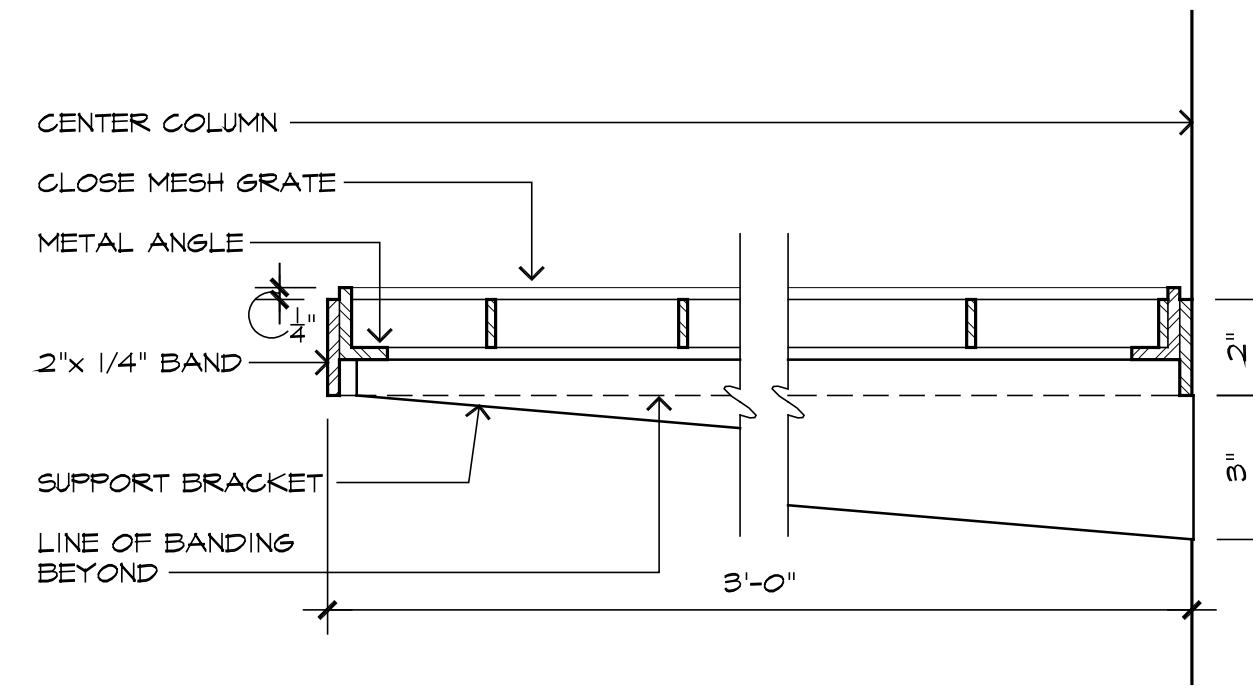


6 DETAIL
SCALE: 3" = 1'-0"

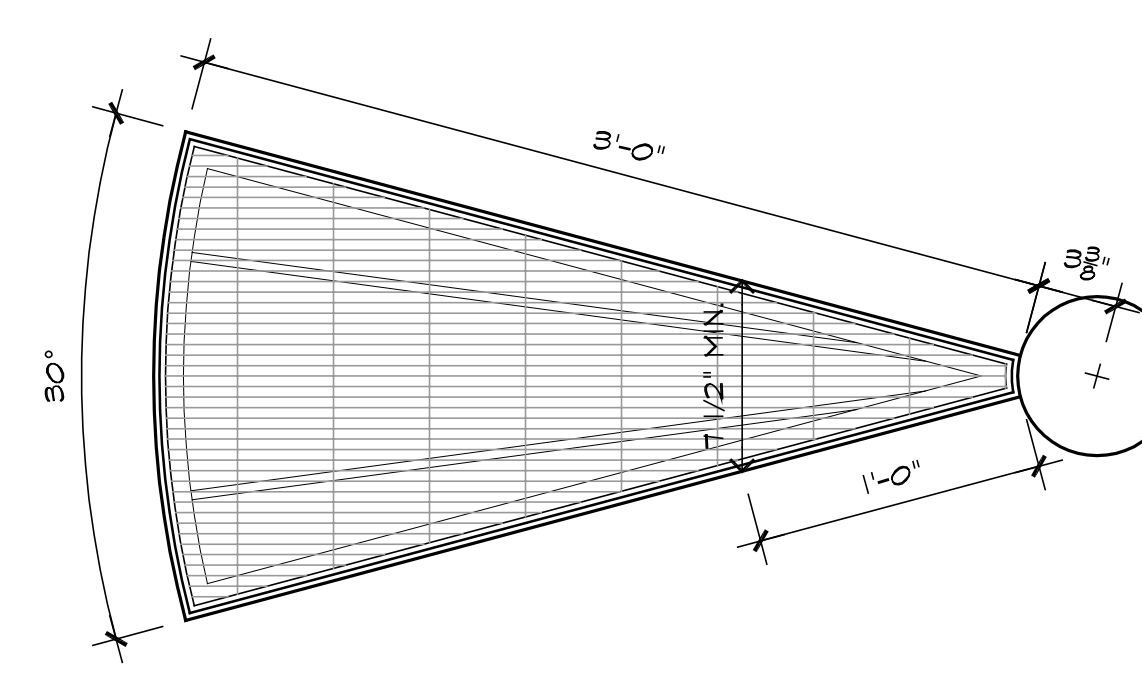


5 DETAIL
SCALE: 1 1/2" = 1'-0"

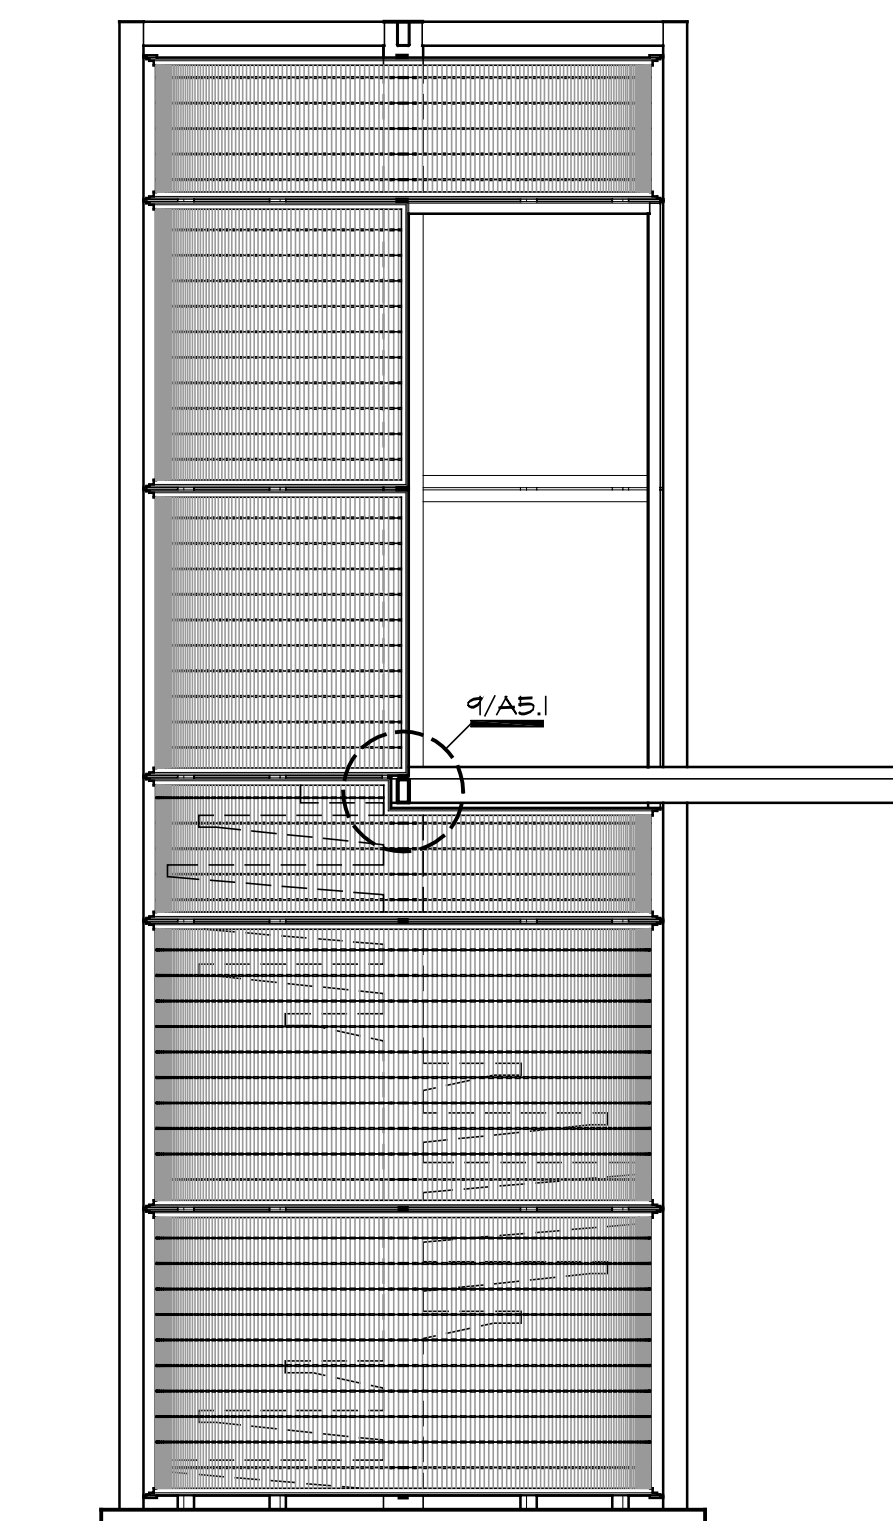


4 ELEVATION/SECTION
SCALE: 3/8" = 1'-0"

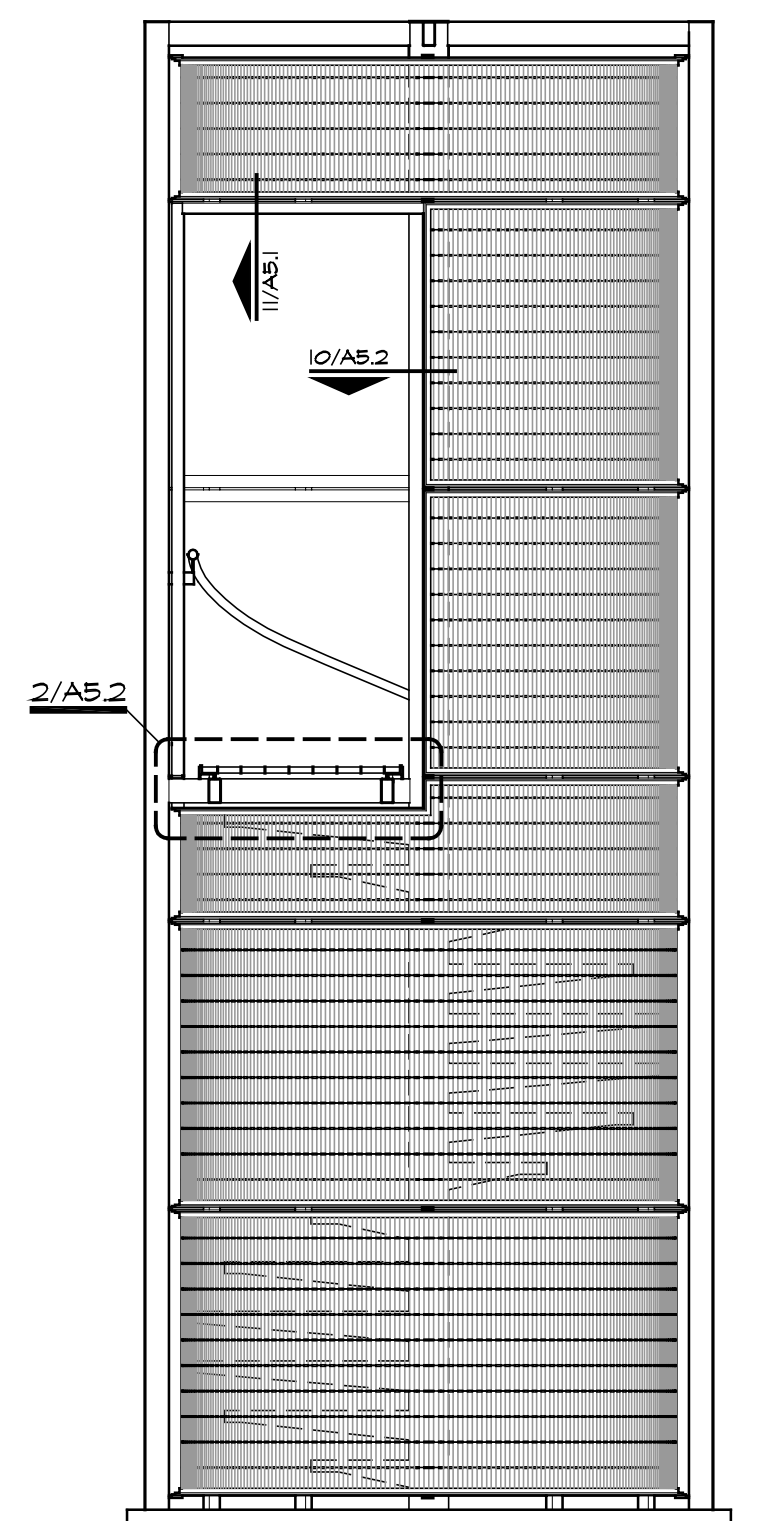

3 ELEV./SECTION
SCALE: 3/8" = 1'-0"

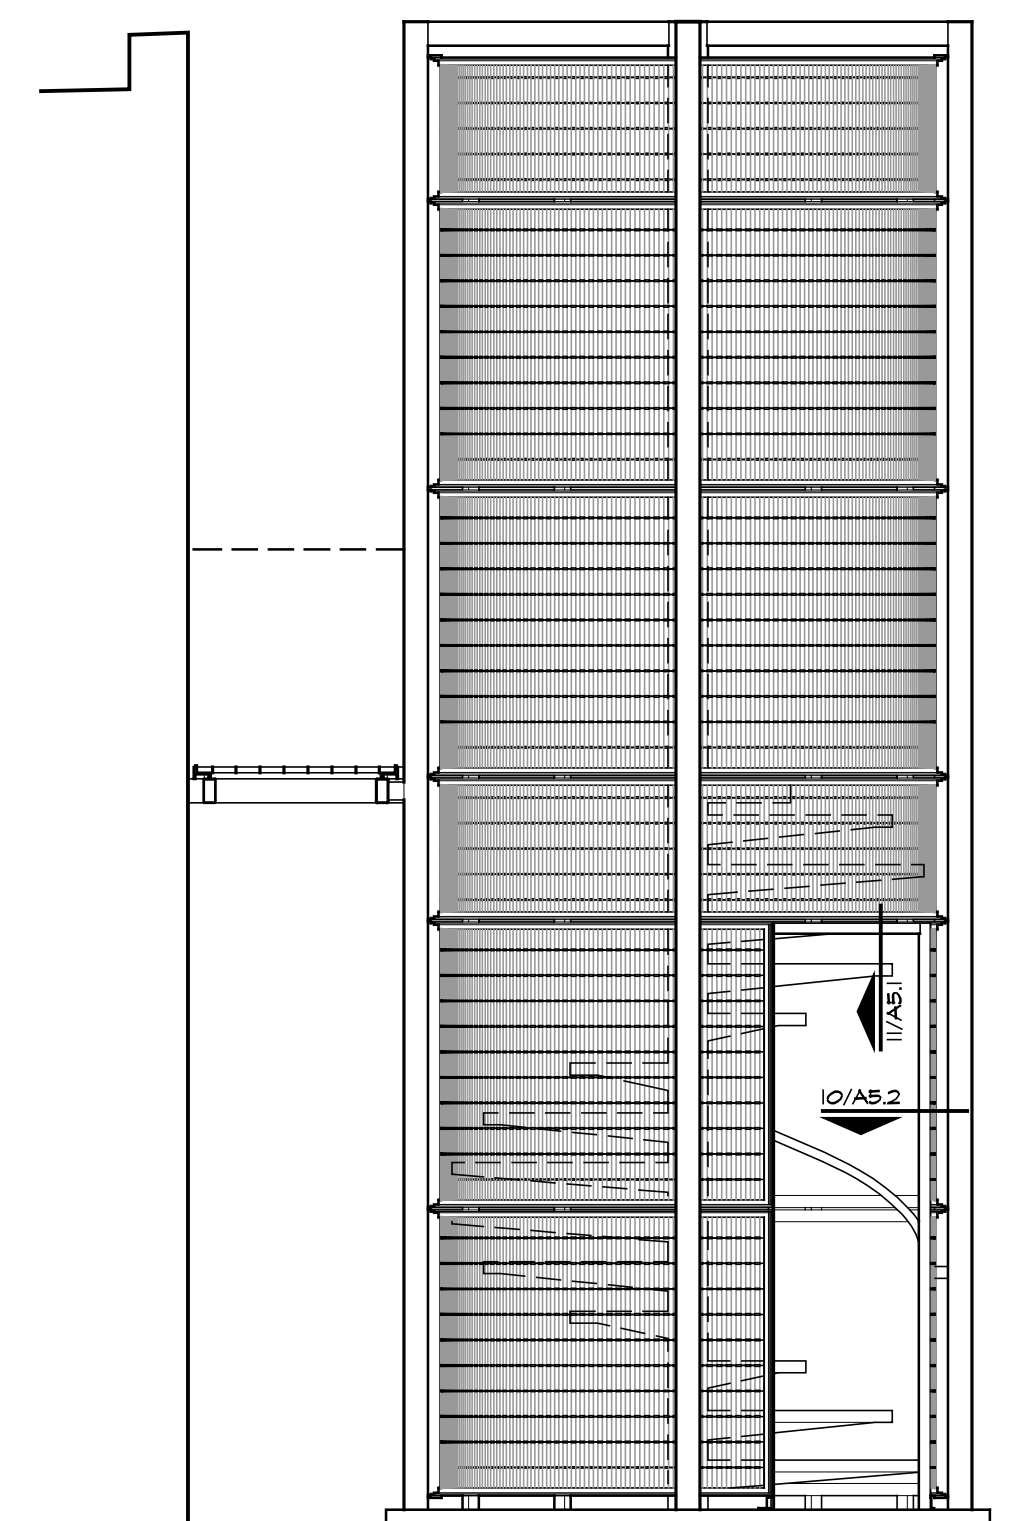

2 ELEVATION/SECTION
SCALE: 3/8" = 1'-0"

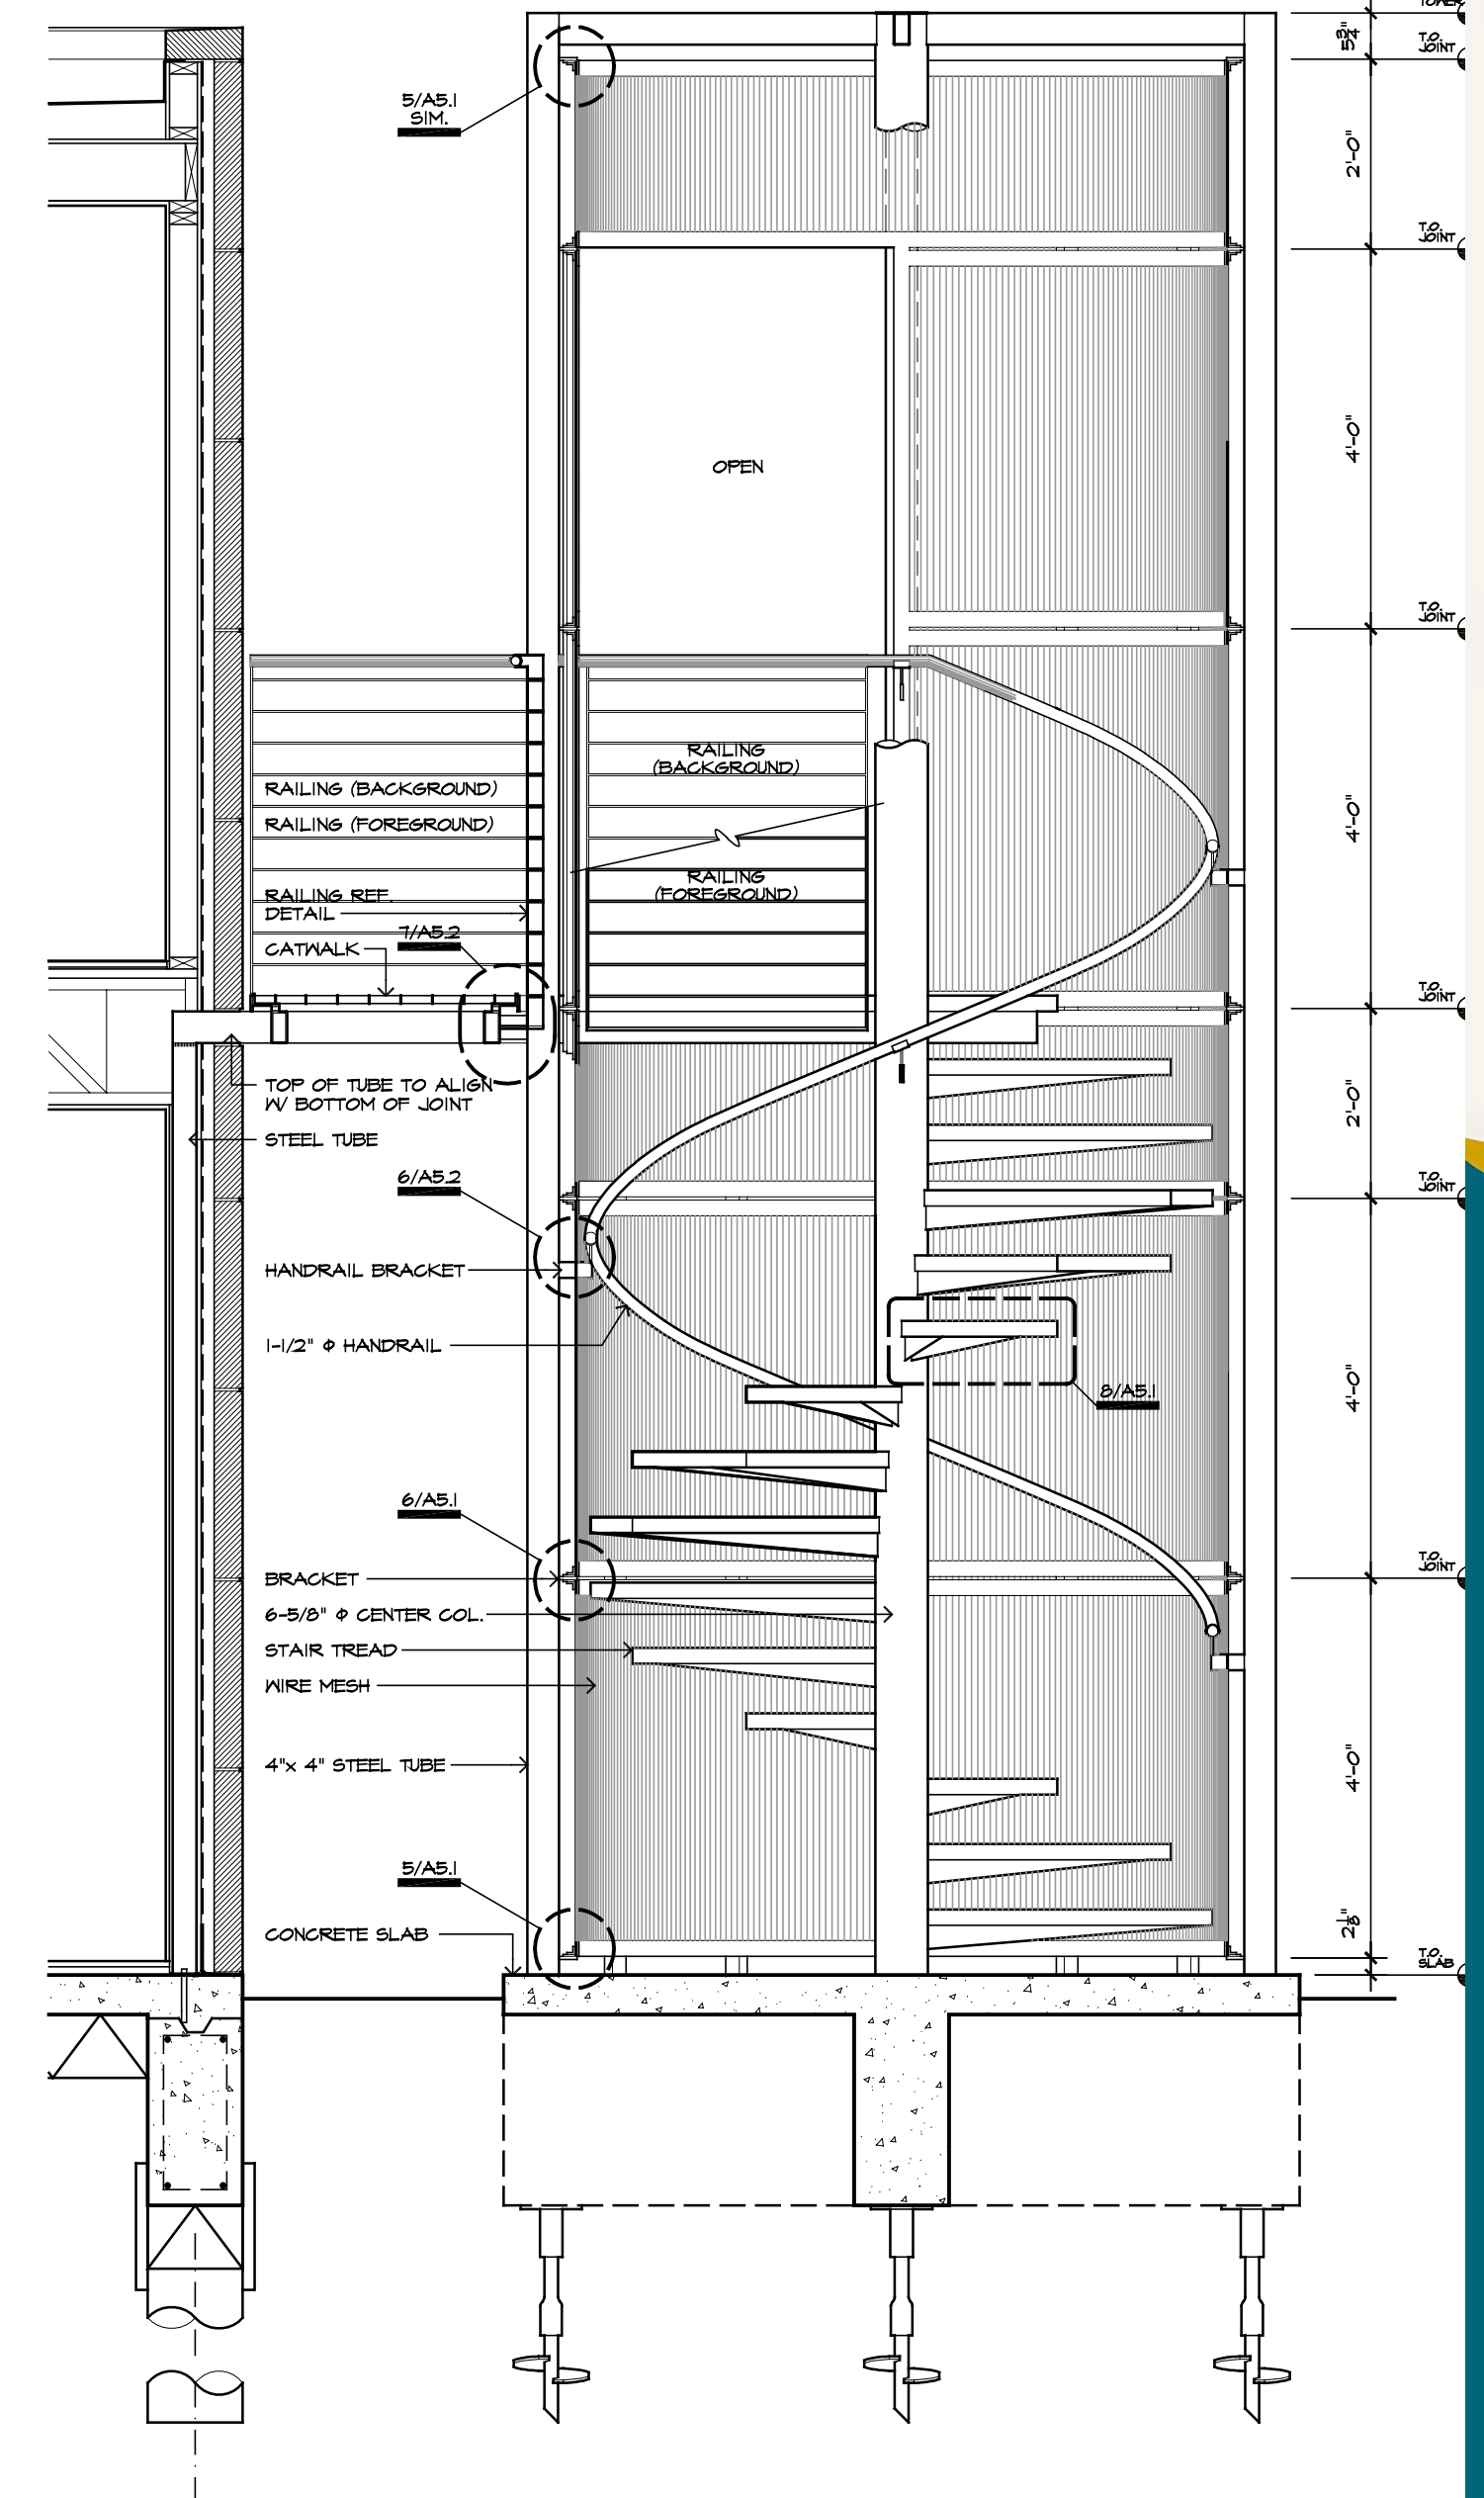

1 WALL SECTION
SCALE: 3/4" = 1'-0"

Need your
project to
look like
this?

Ira
can
do it

iracad
Consulting &
Design

Contact Us

214-717-8407
ira@iracad.com

This design is the intellectual property of Iracad Consulting and Design and is provided for reference only. Unauthorized reproduction, distribution, or use in any form without written permission is strictly prohibited. All rights reserved.