


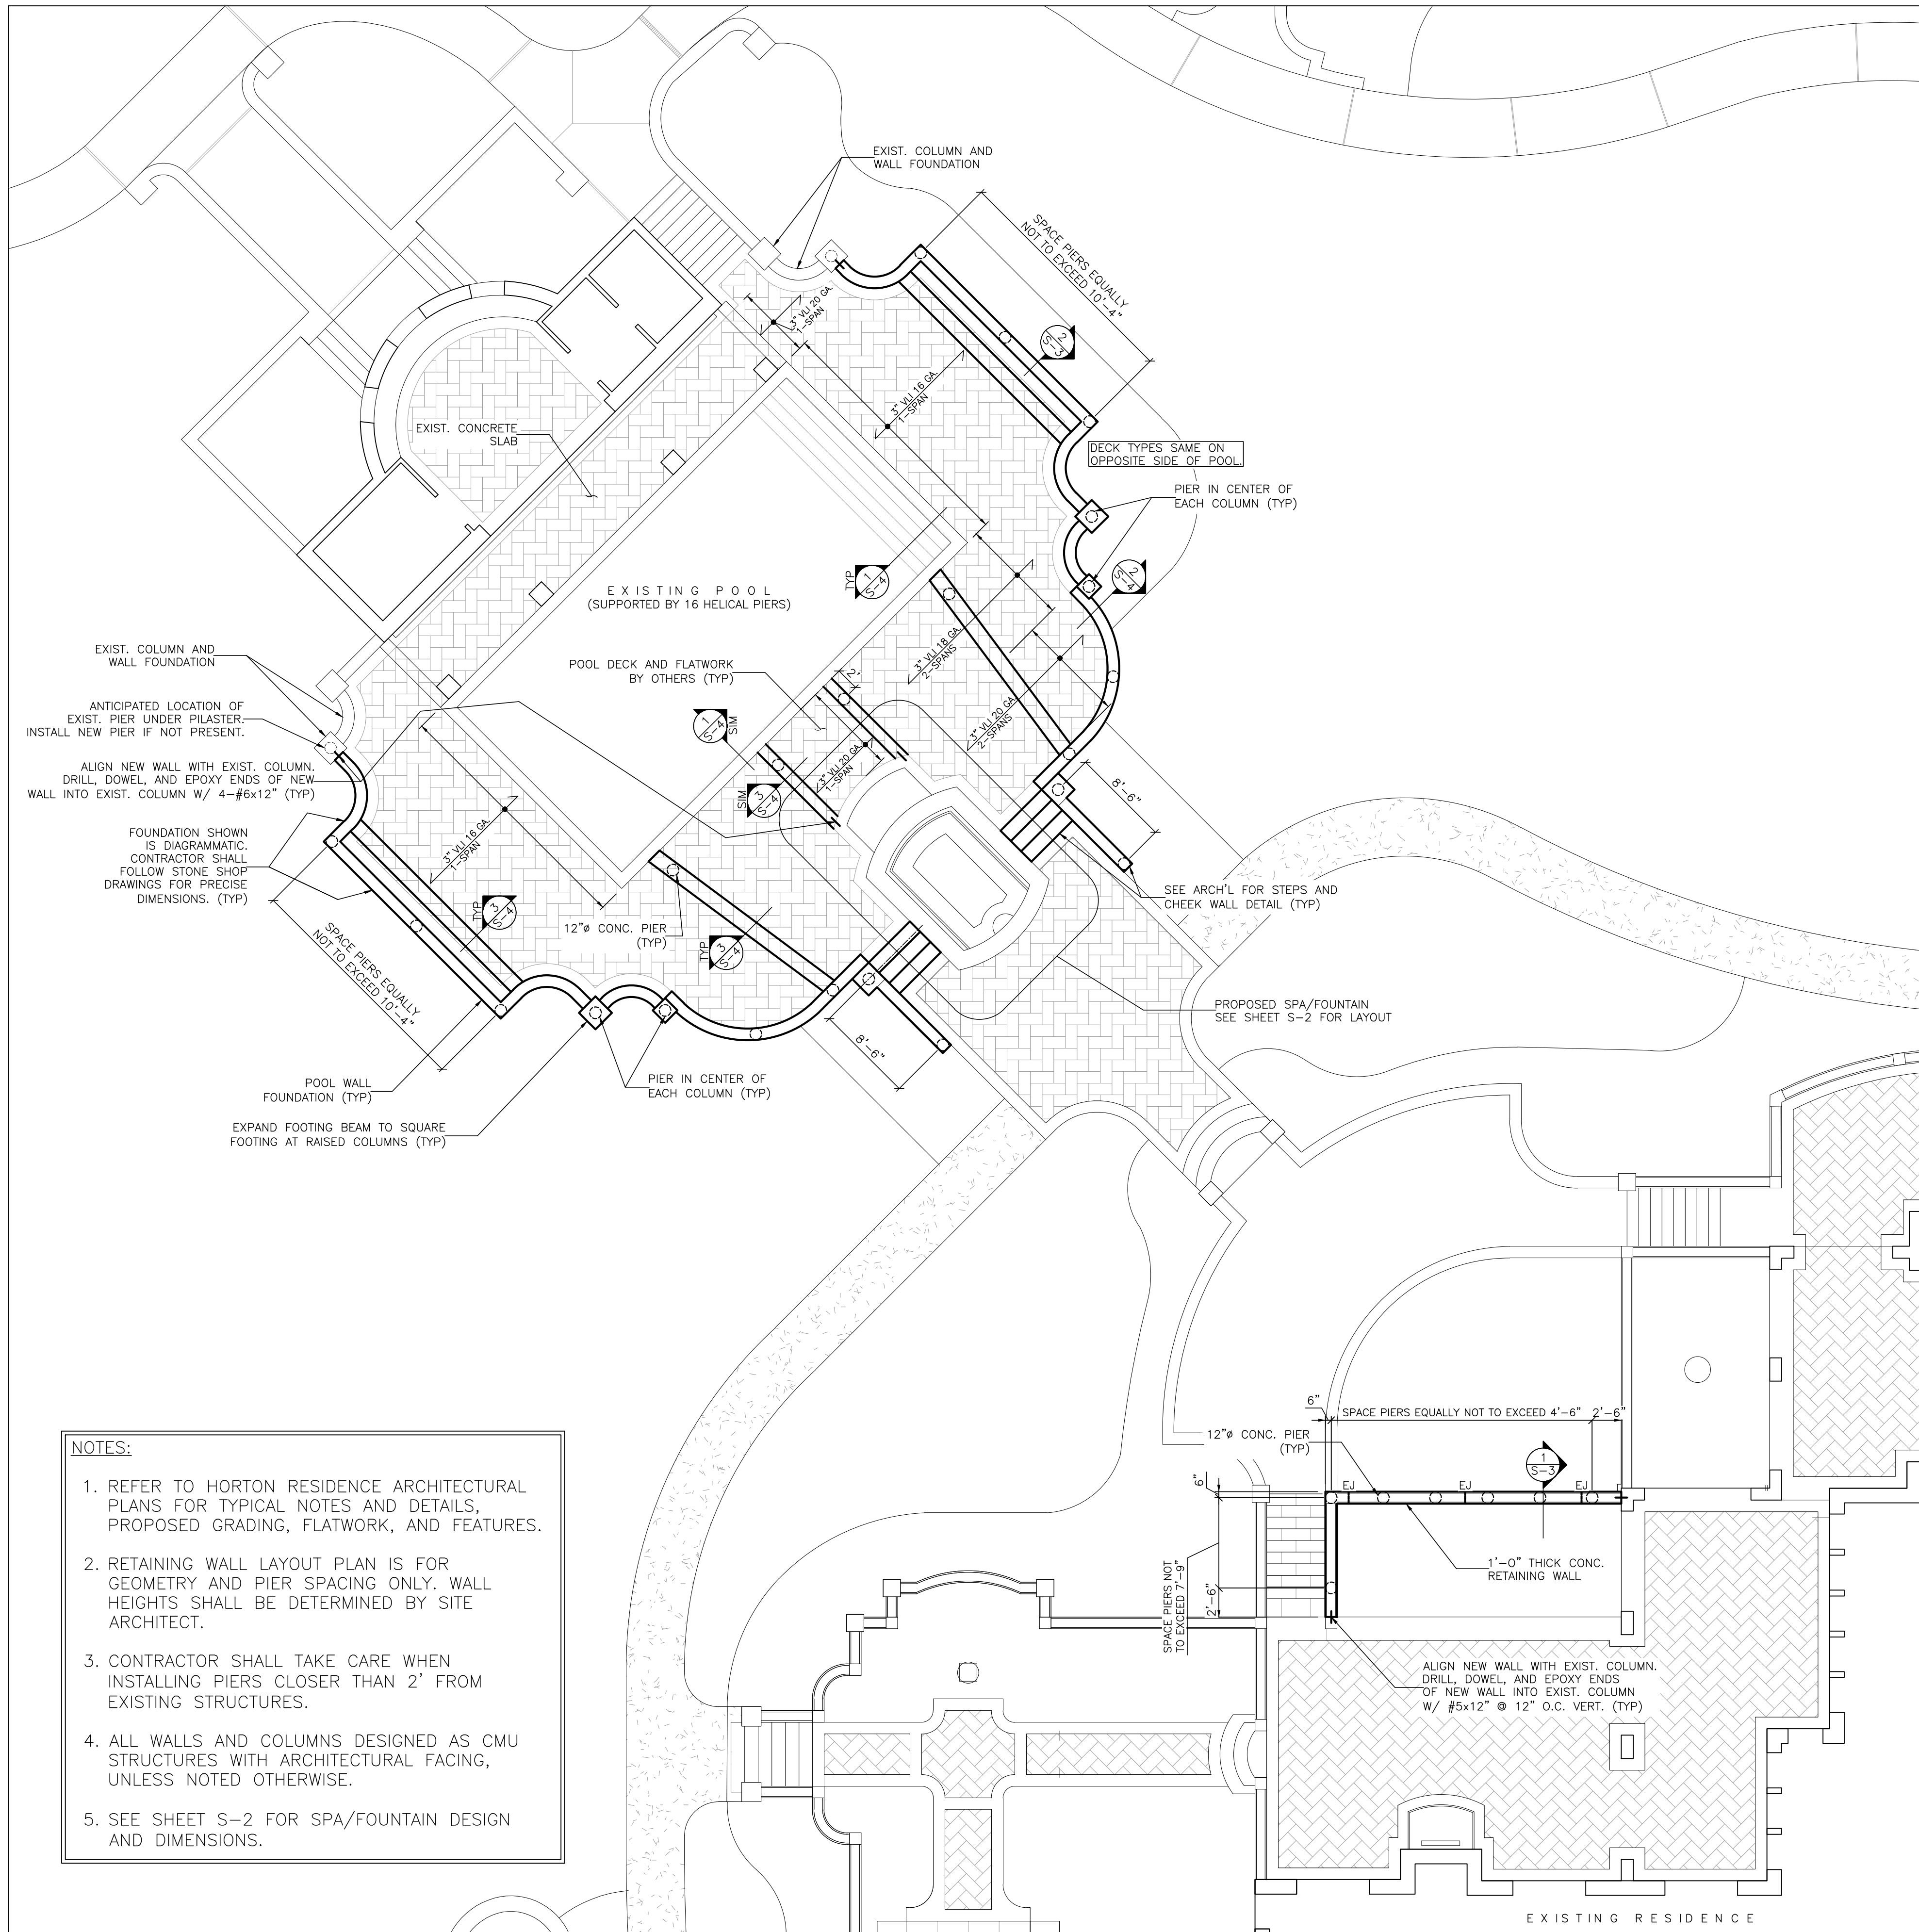


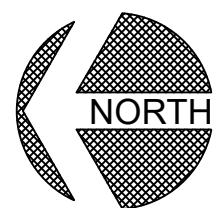



- NOTES:
1. REFER TO HORTON RESIDENCE ARCHITECTURAL PLANS FOR TYPICAL NOTES AND DETAILS, PROPOSED GRADING, FLATWORK, AND FEATURES.
 2. RETAINING WALL LAYOUT PLAN IS FOR GEOMETRY AND PIER SPACING ONLY. WALL HEIGHTS SHALL BE DETERMINED BY SITE ARCHITECT.
 3. CONTRACTOR SHALL TAKE CARE WHEN INSTALLING PIERS CLOSER THAN 2' FROM EXISTING STRUCTURES.
 4. ALL WALLS AND COLUMNS DESIGNED AS CMU STRUCTURES WITH ARCHITECTURAL FACING, UNLESS NOTED OTHERWISE.
 5. SEE SHEET S-2 FOR SPA/FOUNTAIN DESIGN AND DIMENSIONS.

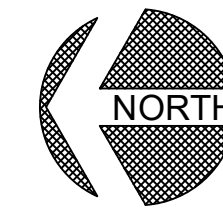

SITE RETAINING WALL AND POOL DECK LAYOUT PLAN – NORTH
SCALE: 1/8" = 1'-0"

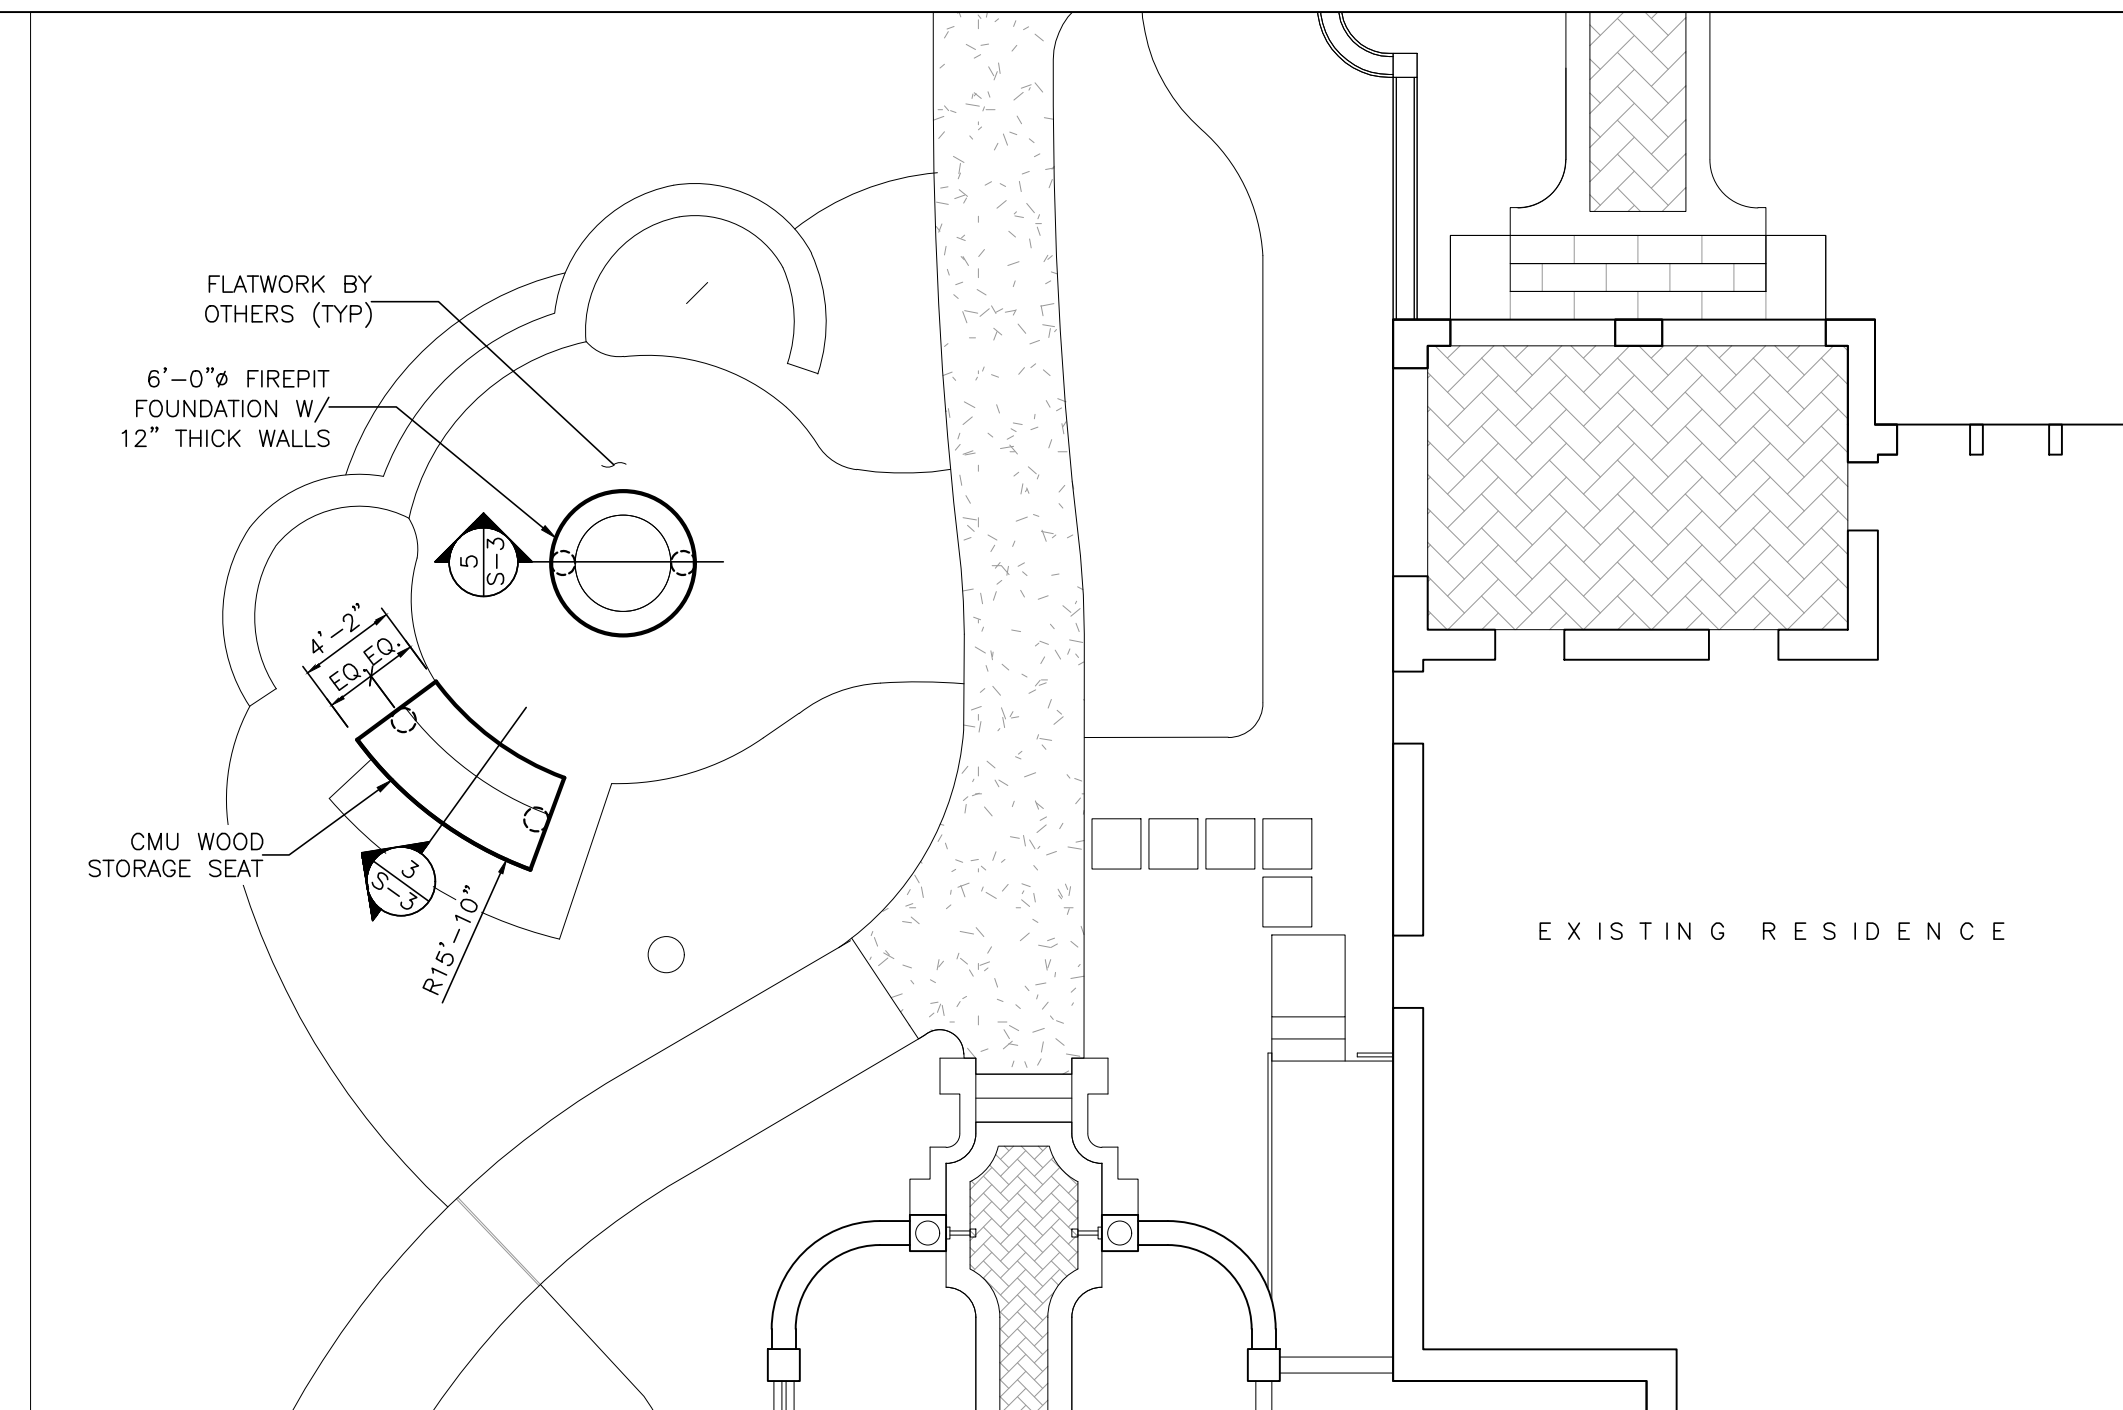

FIREPIT PLAN
SCALE: 1/8" = 1'-0"

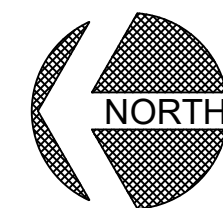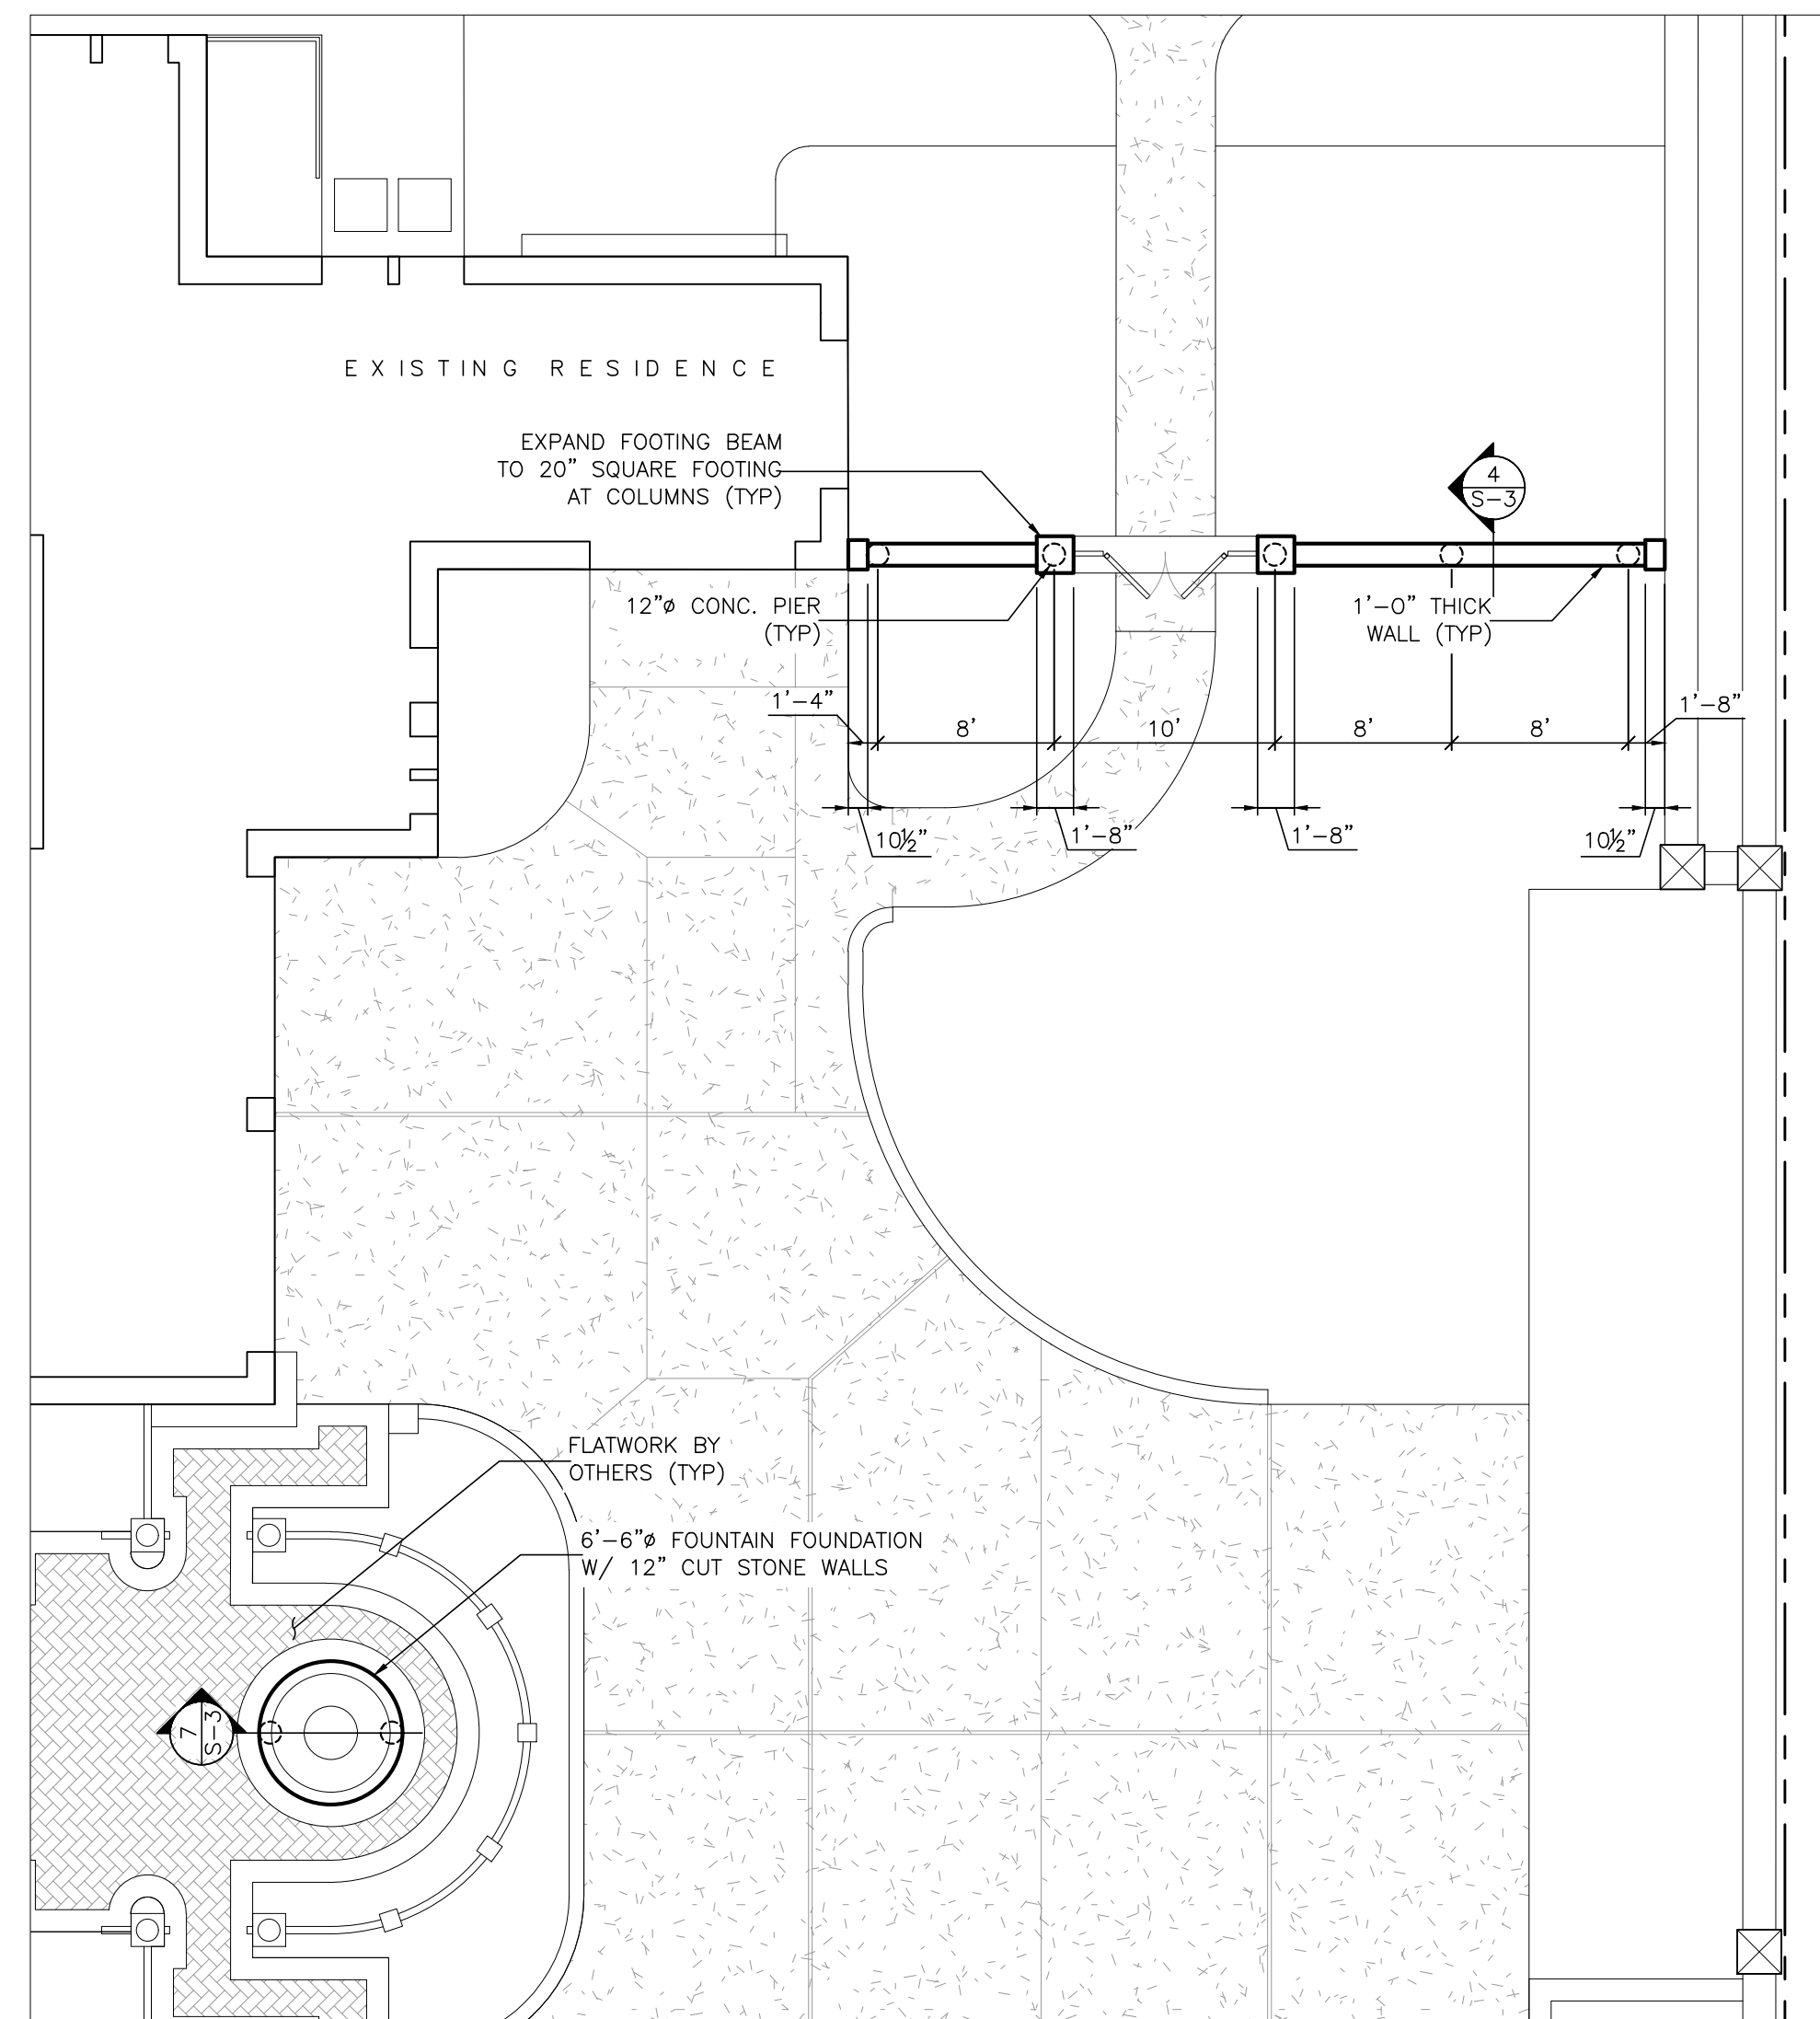

ENTRY ARBOR PLAN – SOUTH
SCALE: 1/8" = 1'-0"

Need your
project to
look like
this?

Ira
can
do it

iracad
Consulting &
Design

Contact Us

214-717-8407
ira@iracad.com

This design is the intellectual property of iracad Consulting and Design and is provided for reference only. Unauthorized reproduction, distribution, or use in any form without written permission is strictly prohibited. All rights reserved.